

województwo: świętokrzyskie  
powiat: kielecki  
gmina: 260403\_4 Chęciny - miasto  
obiekt: 0001 OBR.01  
ulica: Dobrzańska  
dzielnica: 291/1, 291/2, 291/3, 291/4, 291/5, 291/6, 291/7, 292, 293/1, 293/2, 293/3, 293/4, 293/5, 293/6, 293/7, 293/8, 293/9, 293/10, 293/11, 293/12, 294/5, 294/6, 299/2, 299/3, 299/4, 300/1, 300/3, 301/1  
Numer sekcji: 7.14.2.16.19.1.4, 7.14.2.16.19.1.4, 7.14.2.16.19.2.1

Identyfikator zgłoszenia: GN-III.664.0.84.24.2024

Mapa niniejsza, zaktualizowana w obrębie dżdżek nr 291/1, 291/2, 291/3, 291/4, 291/5, 291/6, 291/7, 292, 293/1, 293/2, 293/3, 293/4, 293/5, 293/6, 293/7, 293/8, 293/9, 293/10, 293/11, 293/12, 294/5, 294/6, 299/2, 299/3, 299/4, 300/1, 300/3, 301/1, sporządzona na podstawie danych numerycznych udostępnionych w Powiatowym Ośrodku Dokumentacji Geodezyjnej i Kartograficznej w Kielcach oraz pomiaru bezpośredniego geodety uprawniony inż. Marcin Pitał.


**UWAGA!**  
Nie badano obciążenia służebnością gruntu, przedmiotowych dżdżek.  
Granice nieruchomości i użytki przyjęte według ewidencji gruntów.  
Granice dżdżek spełniają wymogi dokumentacyjne.  
Obszar aktualizacji oznaczono linią czerwoną.  
Elementy ZUDP oznaczono linią przerwaną, w kolorze przypisany do rodzaju sieci.  
Na niniejszej mapie symbolami △-△ oznaczono nieprzekraczalne linie zabudowy.  
Na niniejszej mapie symbolom - - - - - oznaczono linie ograniczające tereny o różnym przeznaczeniu.  
Na niniejszej mapie opisano przeznaczenie terenu zgodnie z miejscowym planem zagospodarowania terenu.  
Nie wykluje się istnienia w terenie innych niż wskazanych na niniejszej mapie urządzeń podziemnych, które nie były zgłoszone do inwentaryzacji lub o których braku jest informacji w instytucjach branżowych.

Układ współrzędnych prostokątnych płaskich: „2000..”  
Układ wysokościowy: „PL-EVRF2007-NH..”

Kielce, dnia 09.11.2024 r.

„GEO-MAR“ USŁUGI GEODEZYJNE  
inż. Marcin Pitał  
nr. upr. 2192/24  
25-546 Kielce, ul. Z. Nalewki 5/27  
NIP 527-112-71-97 REGON 260407852

Oświadczam, że niniejszy dokument został sporządzony w wyniku prac geodezyjnych i kartograficznych, których rezultaty zatwierdzone są operatorem technicznym pozytywnie zweryfikowane.	
Jestem świadomy odpowiedzialności karmy za żelazne oświadczenie.	
Organ prowadzący jednostkę podlegającą sprawozdaniu	STAROSTA KIELECKI
Został geodezyjny i kartograficzny	GK-III.664.0.84.24.2024
Numer aktu sporządzenia dokumentu potwierdzającego pozytywny wynik weryfikacji	GN-III.664.0.84.24.2024_1 z dnia 21.11.2024 r.
Wykonawca prac geodezyjnych i kartograficznych numer uprawnienia do prowadzenia kierownika prac geodezyjnych	GEODETA UPRAWIONY inż. Marcin Pitał nr. upr. 2192/24

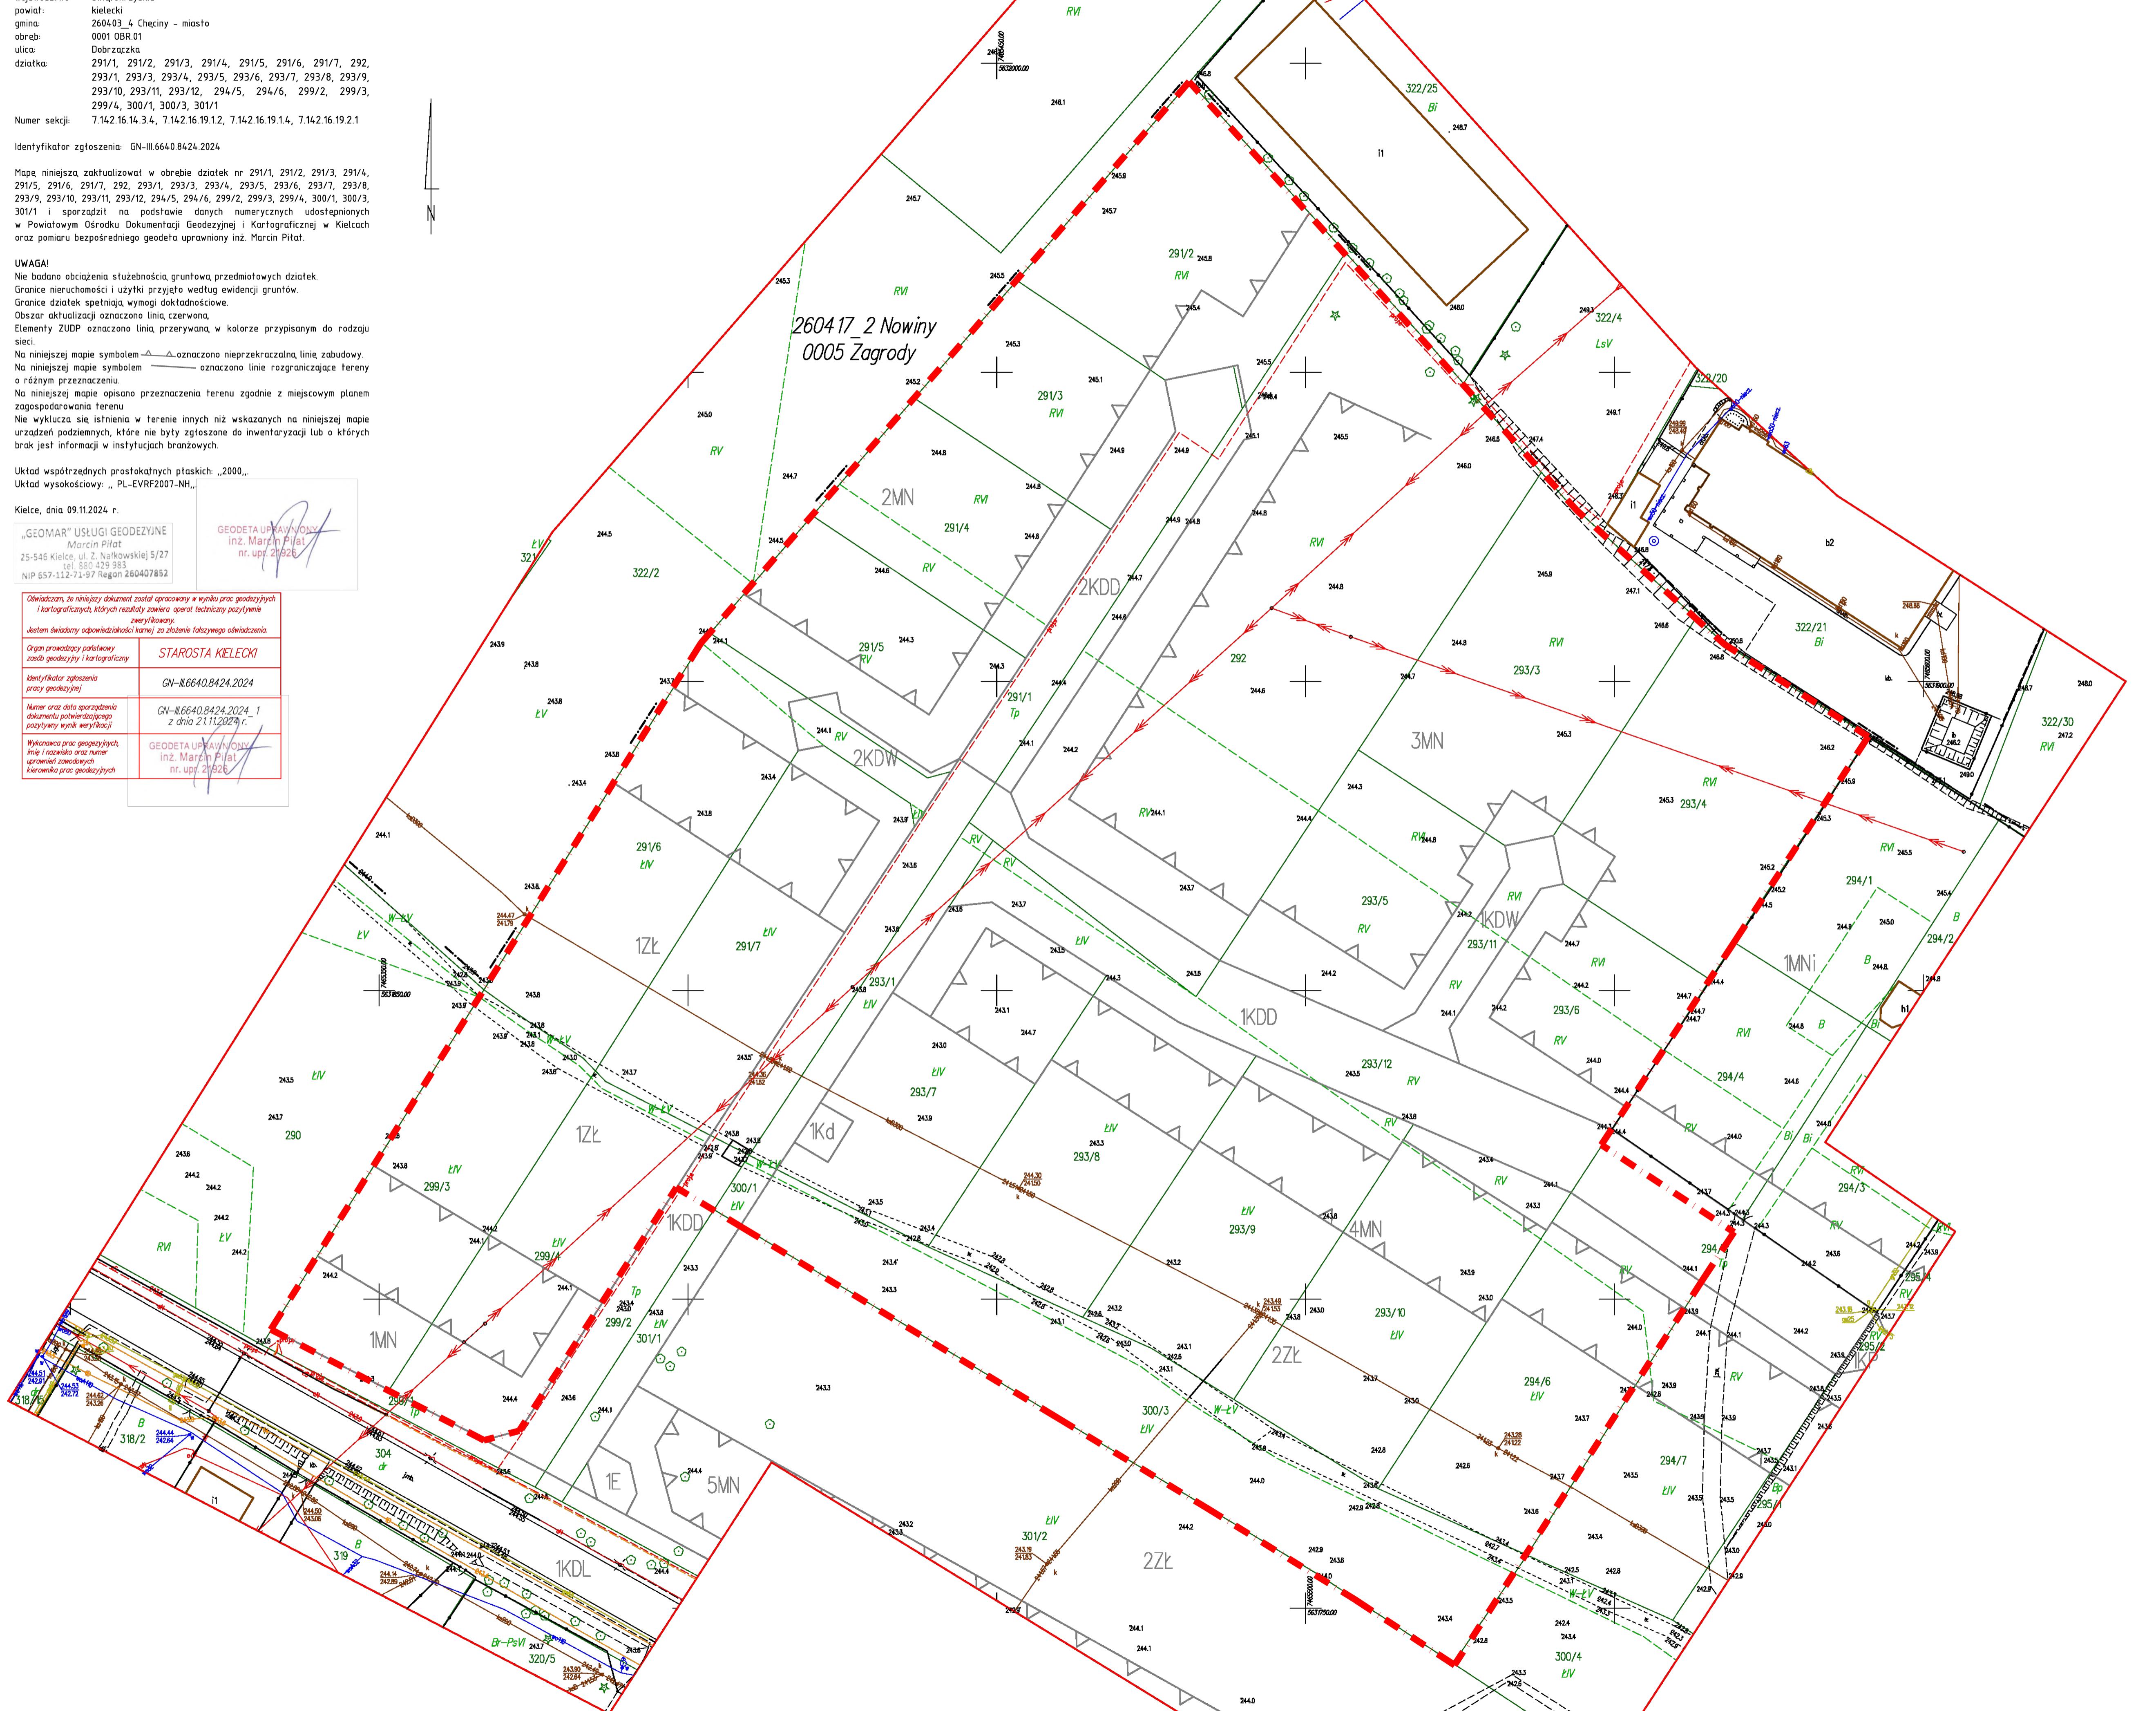

## MAPA DO CELÓW PROJEKTOWYCH

SKALA 1:500

województwo: świętokrzyskie  
powiat: kielecki  
gmina: 260403\_4 Chęciny - miasto  
obręb: 0001 OBR.01  
ulica: Dobrzańska  
dzielnica: 291/1, 291/2, 291/3, 291/4, 291/5, 291/6, 291/7, 292, 293/1, 293/2, 293/3, 293/4, 293/5, 293/6, 293/7, 293/8, 293/9, 293/10, 293/11, 293/12, 294/5, 294/6, 299/2, 299/3, 299/4, 300/1, 300/3, 301/1, 300/1, 300/3, 301/1  
Numer sekcji: 7.14.2.16.14.3.4, 7.14.2.16.19.1.2, 7.14.2.16.19.1.4, 7.14.2.16.19.2.1  
Identyfikator zgłoszenia: GN-III.6640.8424.2024

Mapa niniejsza, zaktualizowana w obrębie działy nr 291/1, 291/2, 291/3, 291/4, 291/5, 291/6, 291/7, 292, 293/1, 293/2, 293/3, 293/4, 293/5, 293/6, 293/7, 293/8, 293/9, 293/10, 293/11, 293/12, 294/5, 294/6, 299/2, 299/3, 299/4, 300/1, 300/3, 301/1 i sporządzona na podstawie danych numerycznych udostępnionych w Powiatowym Ośrodku Dokumentacji Geodezyjnej i Kartograficznej w Kielcach oraz pomiaru bezpośredniego geodety uprawniony inż. Marcin Pilit.

**UWAGA!**  
Nie badano obciążenia służebnością gruntuową przedmiotowych działek.  
Granice nieruchomości i użytki przyjęte według ewidencji gruntów.  
Granice działy spełniają wymogi dokumentacyjne.  
Obszar aktualizacji oznaczono linią czerwoną.  
Elementy ZUD oznaczono linią przerwaną, w kolorze przypisany do rodzaju sieci.  
Na niniejszej mapie symbolami △, ▲ oznaczono nieprzekraczalne linie zabudowy.  
Na niniejszej mapie symbolami — oznaczono linie ograniczające tereny o różnym przeznaczeniu.  
Na niniejszej mapie opisano przeznaczenia terenu zgodnie z miejscowym planem zagospodarowania terenu.

Nie wykluje się istniejące w terenie innych niż wskazanych na niniejszej mapie urządzenia podziemne, które nie były zgłoszone do inwentaryzacji lub u których brak jest informacji w instytucjach branżowych.

Układ współrzędnych płaskich: „2000..”

Układ wysokościowy: „PL-EVR2007-NH..”

Kielce, dnia 09.11.2024 r.

„GEOFAR” USŁUGI GEODEZYJNE  
inż. Marcin Pilit  
nr. upr. 21924  
25-546 Kielce, ul. Z. Nalewki 5/27  
NIP 527-112-71-9 REGON 260407852

Oświadczenie, że niniejszy dokument został sporządzony w wyniku prac geodezyjnych i kartograficznych, których rezultaty zawiera operat techniczny pozytywnie zweryfikowany.  
Jestem świadom odpowiadalności kieruję do końca fazy projektowej oświadczenie:  
Organ prowadzący pozwolenie: STAROSTA KIELECKI  
Zespoły geodezyjno-kartograficzne: inż. Marcin Pilit  
nr. upr. 21924  
Identyfikator zgłoszenia: GN-III.6640.8424.2024  
Numer daty sporządzenia dokumentu potwierdzającego pozytywny wynik weryfikacji: GN-III.6640.8424.2024, 1 z dnia 21.11.2024 r.  
Wykonawca prac geodezyjnych i kartograficznych: inż. Marcin Pilit  
nr. upr. 21924  
Kierownik prac geodezyjnych i kartograficznych: inż. Marcin Pilit  
nr. upr. 21924

Geodeta uprawniony do prowadzenia geodezyjnych i kartograficznych prac: inż. Marcin Pilit  
nr. upr. 21924

Geodeta uprawniony do prowadzenia geodezyjnych i kartograficznych prac: inż. Marcin Pilit  
nr. upr. 21924

Geodeta uprawniony do prowadzenia geodezyjnych i kartograficznych prac: inż. Mar

**LEGENDA**

- PRZEWIDZIENY BUDYNEK
- ZACIENIANIE: CIĘŃ RZUCANY PRZEZ BUDYNEK W DNIU RÓWNONOCY O DANEJ GODZINIE
- PRZESŁANIAJĄCE: MINIMALNA ODLEGŁOŚĆ OD BUDYNKU SĄSIADUJĄCEGO ZAPewnIAJĄCA DOŚWIETLENIE POMIESZCZEŃ PRZENASCZONYCH NA POBYT LUDZI (ODLEGŁOŚĆ WYNIKAJĄCA Z WYSOKOŚCI PRZESŁANIAJĄCEGO)

**ANALIZA CZASU NASŁONECZNIENIA I PRZESŁANIA**  
Podstawa opracowania:  
Rozporządzenie Ministra Infrastruktury z dnia 12.04.2002 (z późniejszymi zmianami) w sprawie warunków technicznych jakim powinny odpowiadać budynki i ich usytuowanie.

Analiza nasłonecznienia pomieszczeń mieszkalnych jest rozpatrywana w przediale czasowym od godziny 7:00 do 17:00. Schemat przedstawia najmniej korzystną sytuację czyli pomieszczenia w parterze.

\* - Wysość budynku od parapetu najniżzej położonego okna.  
W projektowanych mieszkaniach co najmniej jeden pokój jest nasłoneczniony przez co najmniej 3 godziny, zatem jest spełniony warunek minimalnego nasłonecznienia określony w rozporządzeniu.

**ANALIZA PRZESŁANIA**  
Podstawa opracowania:  
Rozporządzenie Ministra Infrastruktury z dnia 12.04.2002 (z późniejszymi zmianami) w sprawie warunków technicznych jakim powinny odpowiadać budynki i ich usytuowanie.

Dla każdego budynku projektowanego i istniejącego na działce sąsiadującej spełniony jest warunek przesłania (między ramionami kąta 60°, wyznaczonymi w płaszczyźnie poziomej z wierzchołkiem usytuowanym w wewnętrzny licu ściany na osi okna pomieszczenia przeznaczonego na pobyt ludzi - mieszkalnego i biurowego, nie znajduje się przesłaniające części tego samego budynku lub innego obiektu przesłaniającego).

**OKREŚLENIE OBSZARU ODDziaŁYWANIA PROJEKTOWANEGO OBIEKTU BUDOWLANEGO ZE WZGŁĘDU NA BEZPIECZNOŚĆ POŻAROWĄ:**  
Analiza usytuowania budynku ze względu na bezpieczeństwo pożarowe dowodzi że projektowane budynki znajdują się w wymaganej odległości min. 8,00 m od budynków istniejących w związku z powyższym warunki bezpieczeństwa pożarowego nie wprawdzie ograniczeń związanych z istniejącym budynkami. Niestety obszar oddziaływania ze względu na bezpieczeństwo pożarowe nie znajduje się na działkach sąsiadujących.

**WNIOSEK:**  
ZGODNIE Z PRZESTAWIONĄ ANALIZĄ ŻADNA Z DZIAŁEK SĄSIEDNICH NIE ZNAJDUJE SIĘ W OBSZARZE ODDziaŁYWANIA OBIEKTÓW GDYŻ PROJEKTOWANE BUDYNEKI NIE ZMIENIAJĄ WARUNKÓW I STANDARDÓW UŻYTKOWYCH W KARZIE ISTNIEJĄcej ZABUDOWY NA DZIAŁKACH SĄSIADUJĄCYCH I DAJE MOŻLIWOŚĆ ZABUDOWY NA DZIAŁKACH NIEZINWESTOWANYCH.

Autor: M. Wysoczański, arch. tel. 22 260 2000, e-mail: m.wysoczanski@architektura.com.pl  
Zakres: analiza oddziaływanie na działki 243/1, 243/2, 243/3, 